
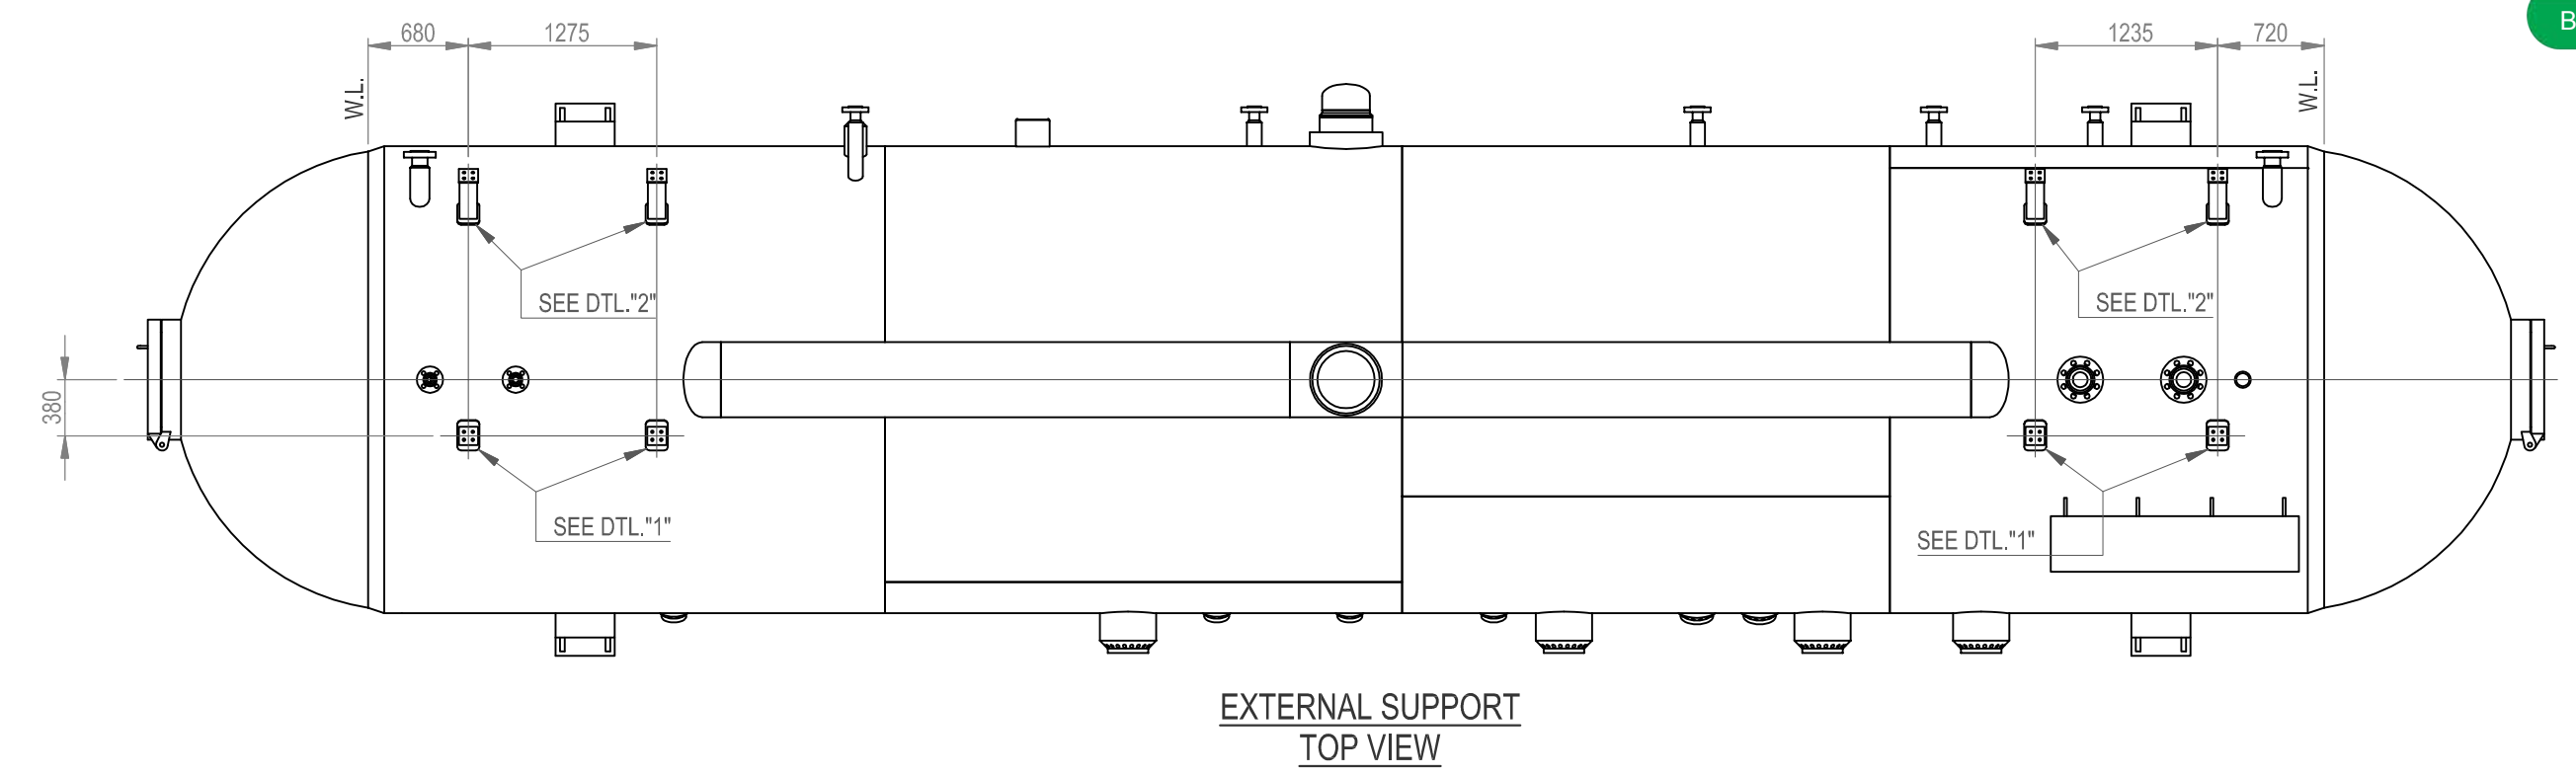
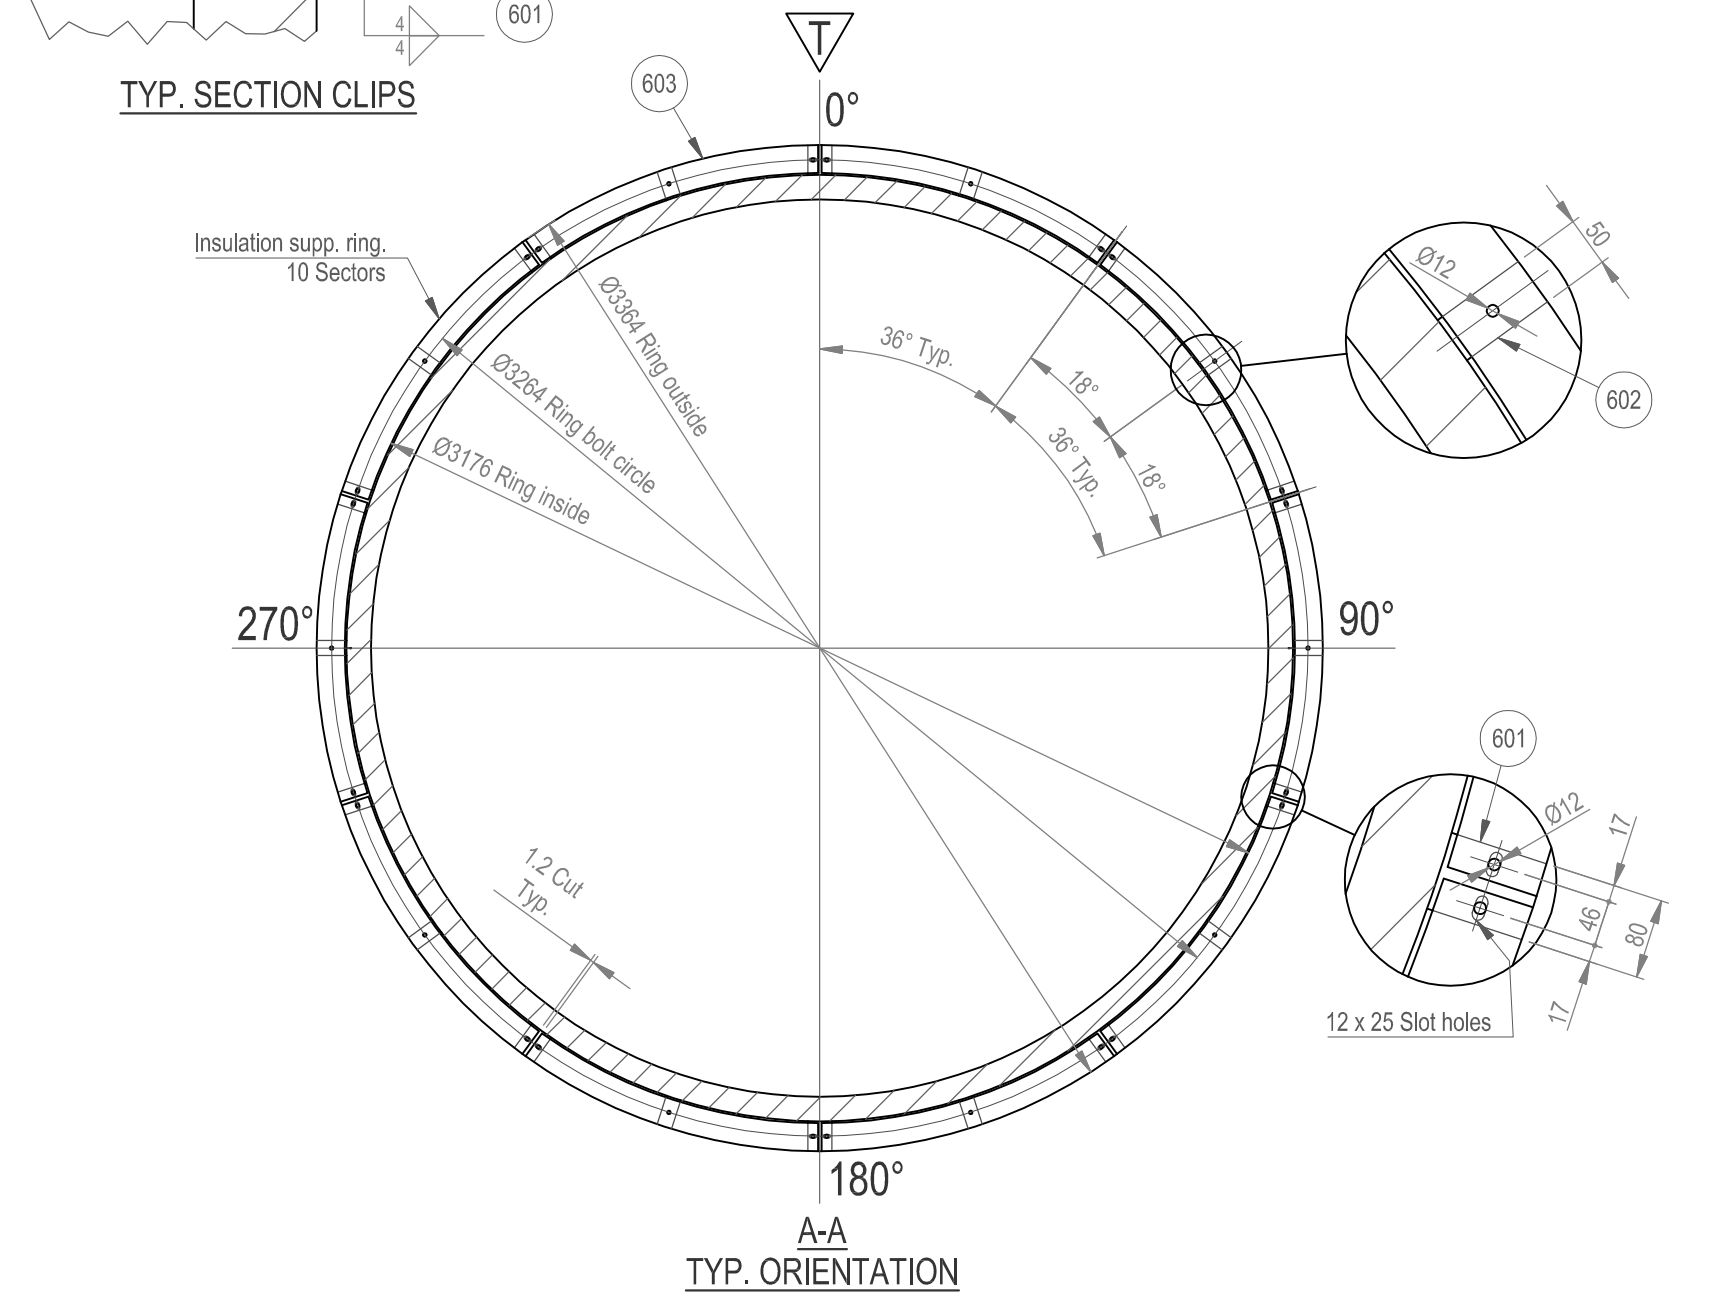
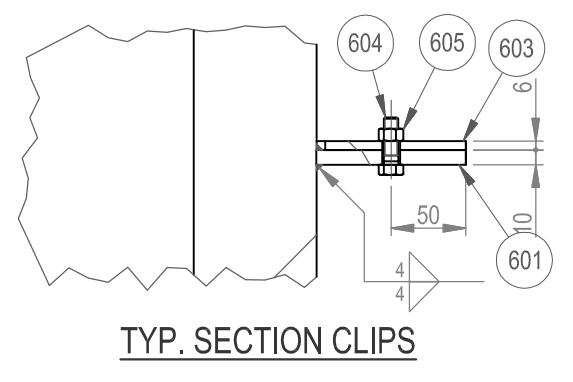
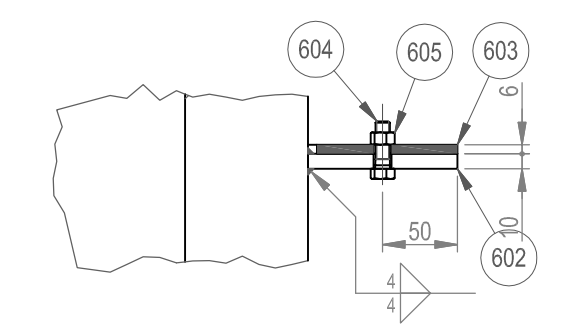
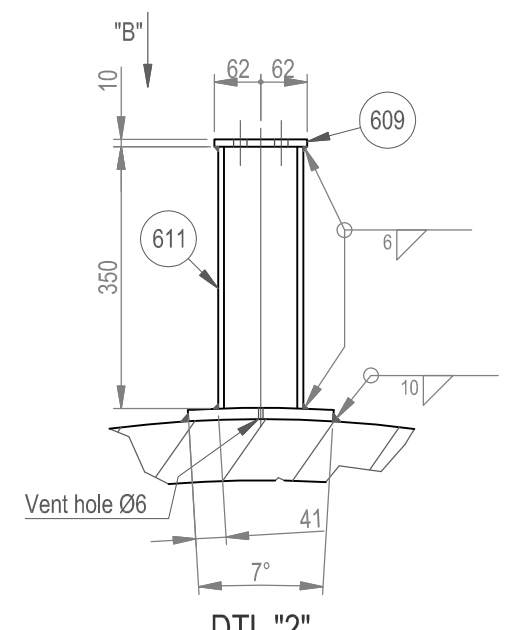
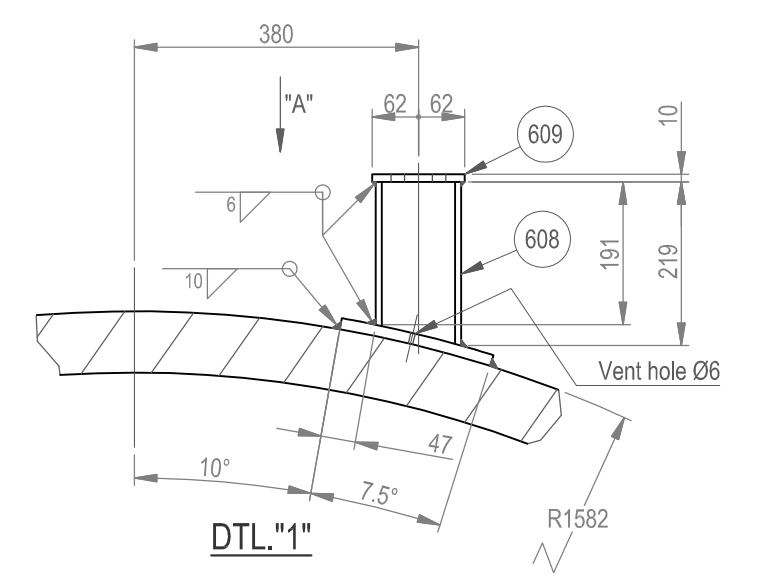
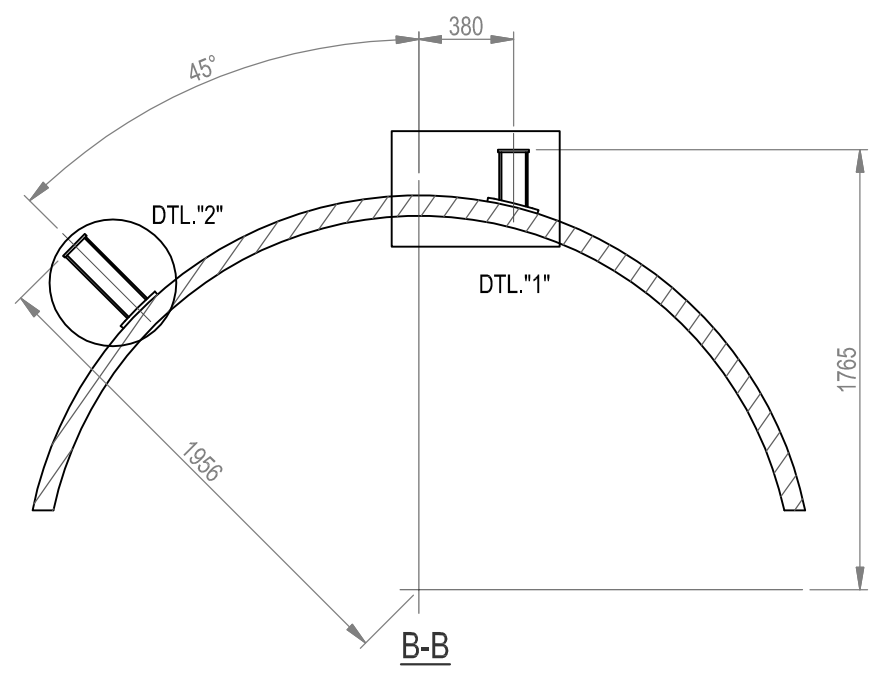
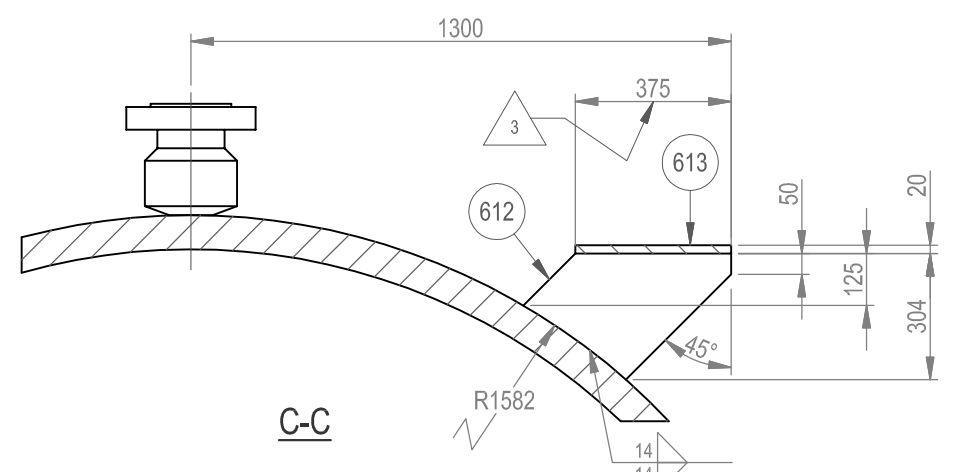
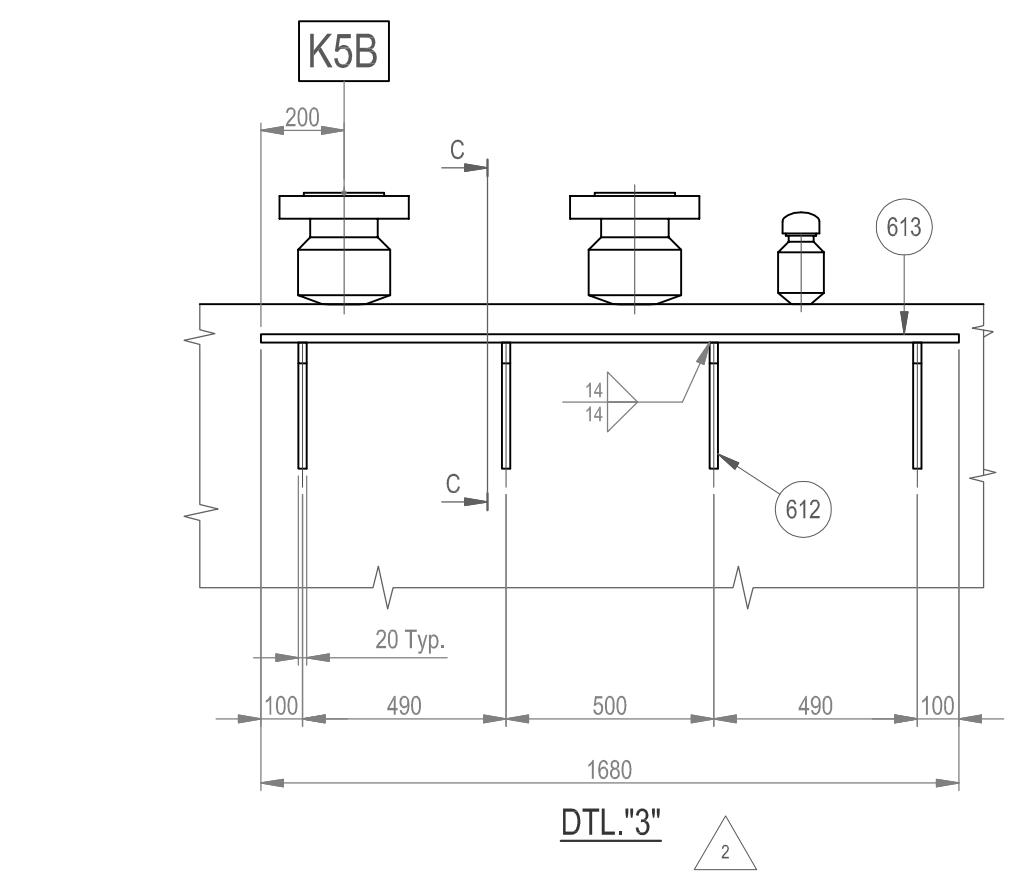


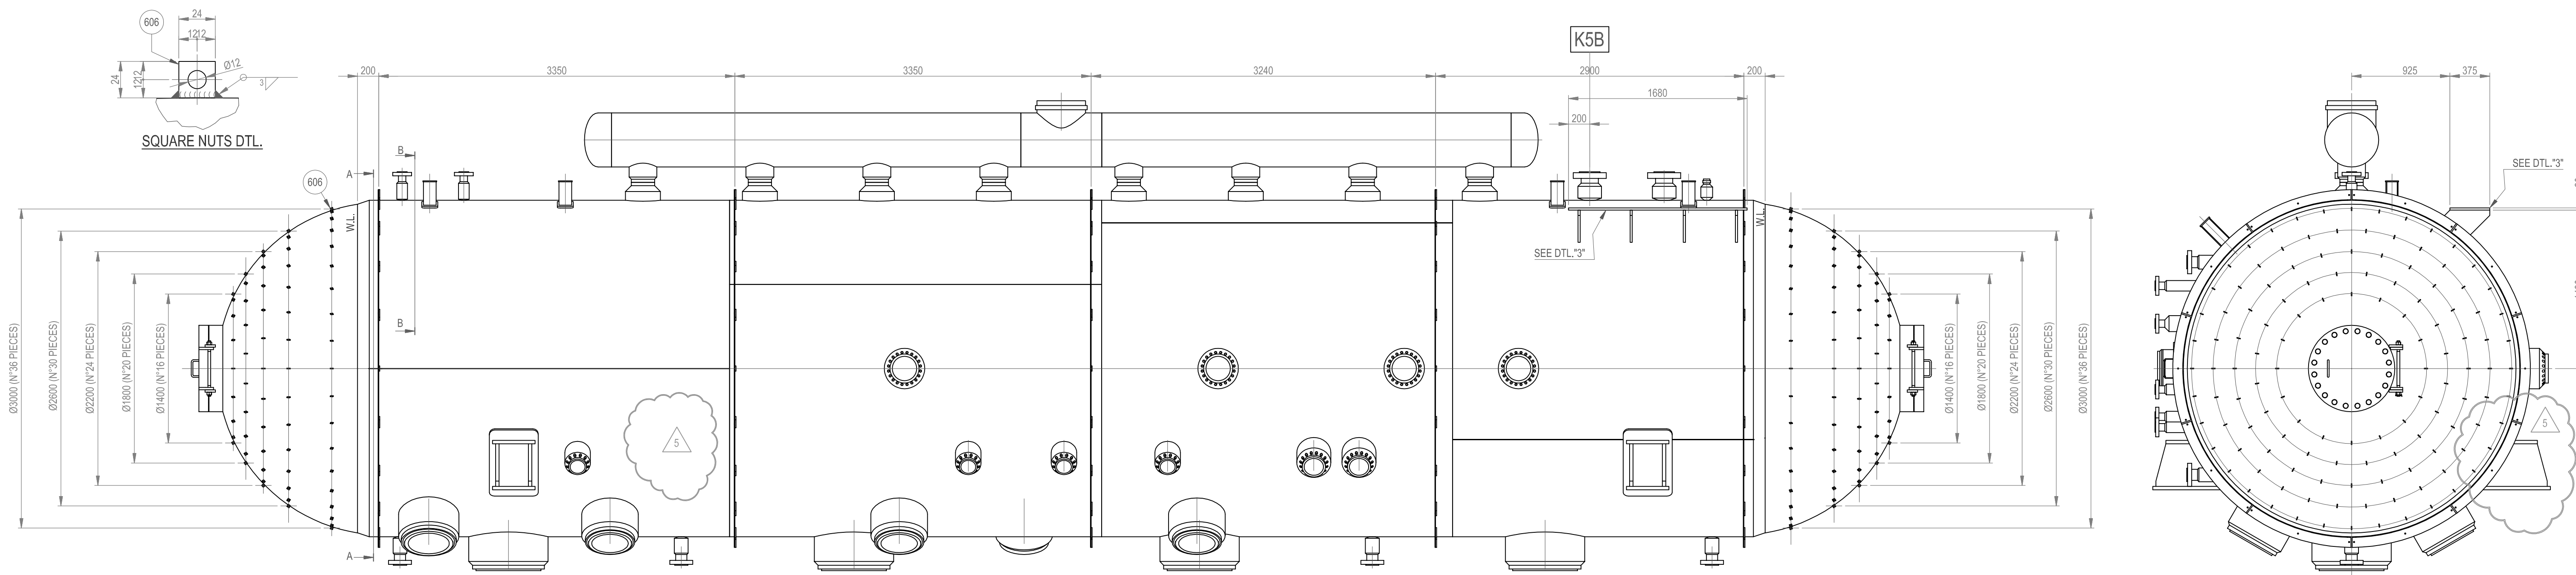

613	Plastra/Plate	1680 x 375 x Thk.20	SA-516 Gr.70N	1	2.2				
612	Nervatura/Stiffening	500 x 304 x Thk.20	SA-516 Gr.70N	4	3.1				
611	Trave di supp./Beam support	HEA 120 Lq.350	S275JR EN10025	4	2.2				
610	Plastra di base/Base plate	195 x 150 x Thk.15	SA-516 Gr.70N	4	3.1				
609	Platto/Plate	130 x 124 x Thk.10	SA-516 Gr.70N	8	2.2				
608	Trave di supp./Beam support	HEA 120 Lq.219	S275JR EN10025	4	2.2				
607	Plastra di base/Base plate	210 x 150 x Thk.15	SA-516 Gr.70N	4	3.1				
606	Dadi supp./Isolamento/Insul. support nuts	24 x 24 x Thk.6	SA-516 Gr.70N	252	3.1				
605	Dadi es./Hex. Nuts	Ø3/8" 16-UNC	C.S.	150	2.2				
604	Bullone/Bolts	Ø3/8" 16-UNC x Lq.35	C.S.	150	2.2				
603	Anello sup. coibentazione/Insul. supp. ring	Ø3364/3176 x Thk.6	SA-516 Gr.70N	50	2.2				
602	Clips sup. coibentazione/Insul. supp. clips	100 x 50 x Thk.10	SA-516 Gr.70N	50	3.1				
601	Clips sup. coibentazione/Insul. supp. clips	100 x 80 x Thk.10	SA-516 Gr.70N	50	3.1				

POS.	DESCRIZIONE/DESCRIPTION	DIMENSIONI/DIMENSIONS	MATERIALE/MATERIAL	Q.TY	CERTIFICATO CERTIFIED	SPARE PARTS	NOTES
3.2	Materiale collaudato da ente ufficiale.						
3.1	Materiale testato da autorità ufficiale.						
2.2	Materiale senza certificato del produttore.						
2.1	Materiale con certificato del produttore.						

Il materiale elencato in distinta è da intendersi valido per N°1 apparecchio.
Quantity indicated on material list are for one shell.

LISTA MATERIALI / MATERIALS LIST

OWNER	LORDEGAN PETROCHEMICAL COMPANY
PROJECT TITLE	LORDEGAN AMMONIA AND UREA PROJECT
CONTRACTOR	HAMPA ENGINEERING CORPORATION
DESIGN ENGINEER	HEIDCO
P.O. NO.	2103-POR-A-IRM-255
REV. NO.	3-D-4201
DOC. NO.	2103-A-YD-255-A1-MD-34
REV.	5

NO.	REVISION	DATE	DESCRIPTION	BY	CHECKED	DATE	DESCRIPTION	BY	CHECKED
5	25/09/2015	Revised as per client comments	Nani	Sarti	Sarti				
4	19/11/2014	Revised where marked & issued (A.S. B.U.I.T.)	Scotti	Pionini	Sarti				
3	02/12/2013	Revision as indicated	Mazzoleni	Sarti	Sarti				
2	26/10/2013	Revision as indicated	Mazzoleni	Sarti	Sarti				

5	25/09/2015	Revised as per client comments	Nani	Sarti	Sarti				
4	19/11/2014	Revised where marked & issued (A.S. B.U.I.T.)	Scotti	Pionini	Sarti				
3	02/12/2013	Revision as indicated	Mazzoleni	Sarti	Sarti				
2	26/10/2013	Revision as indicated	Mazzoleni	Sarti	Sarti				

HEIDCO

By: seraj.mohammad

NO COMMENT

12:07 pm, Oct 22, 2015

SCALE/FORMATO	NO / A1	TITOLO / TITLE	NUMERO APPAR. / NUMBER REQUIRED	SIGLA / ITEM No.	3-D-4201
DATA	29/04/2013	N.A.			
DESIGNATO	Mazzoleni				
DRAWN	Sarti				
CHECKED	Sarti				
APPROVATO	Sarti				

REVISION	DATE	DESCRIPTION	BY	CHECKED	DATE	DESCRIPTION	BY	CHECKED
4	19/11/14	REVISED WHERE MARKED & REISSUED (A.S. B.U.I.T.)	GPM	SP	SS			
3	02/12/13	REVISION AS INDICATED	PM	FG	SS			
2	29/10/13	REVISION AS INDICATED	PM	FG	SS			
1	25/10/13	GENERAL REVISED	PM	FG	SS			
5	25/09/15	REVISED AS PER CLIENT COMMENTS	NL	SS	SS			

OWNER	LORDEGAN PETROCHEMICAL COMPANY
Project	LORDEGAN AMMONIA AND UREA PROJECT
CONTRACTOR	HAMPA ENGINEERING CORPORATION
DESIGN ENGINEER	HEIDCO
TITLE	INSULATION SUPPORT AND WALKWAYS SUPPORT
Project No.	2103-03-500-03
Scale	Vendor
Sheet of	2103-A-YD-255-A1-MD-034