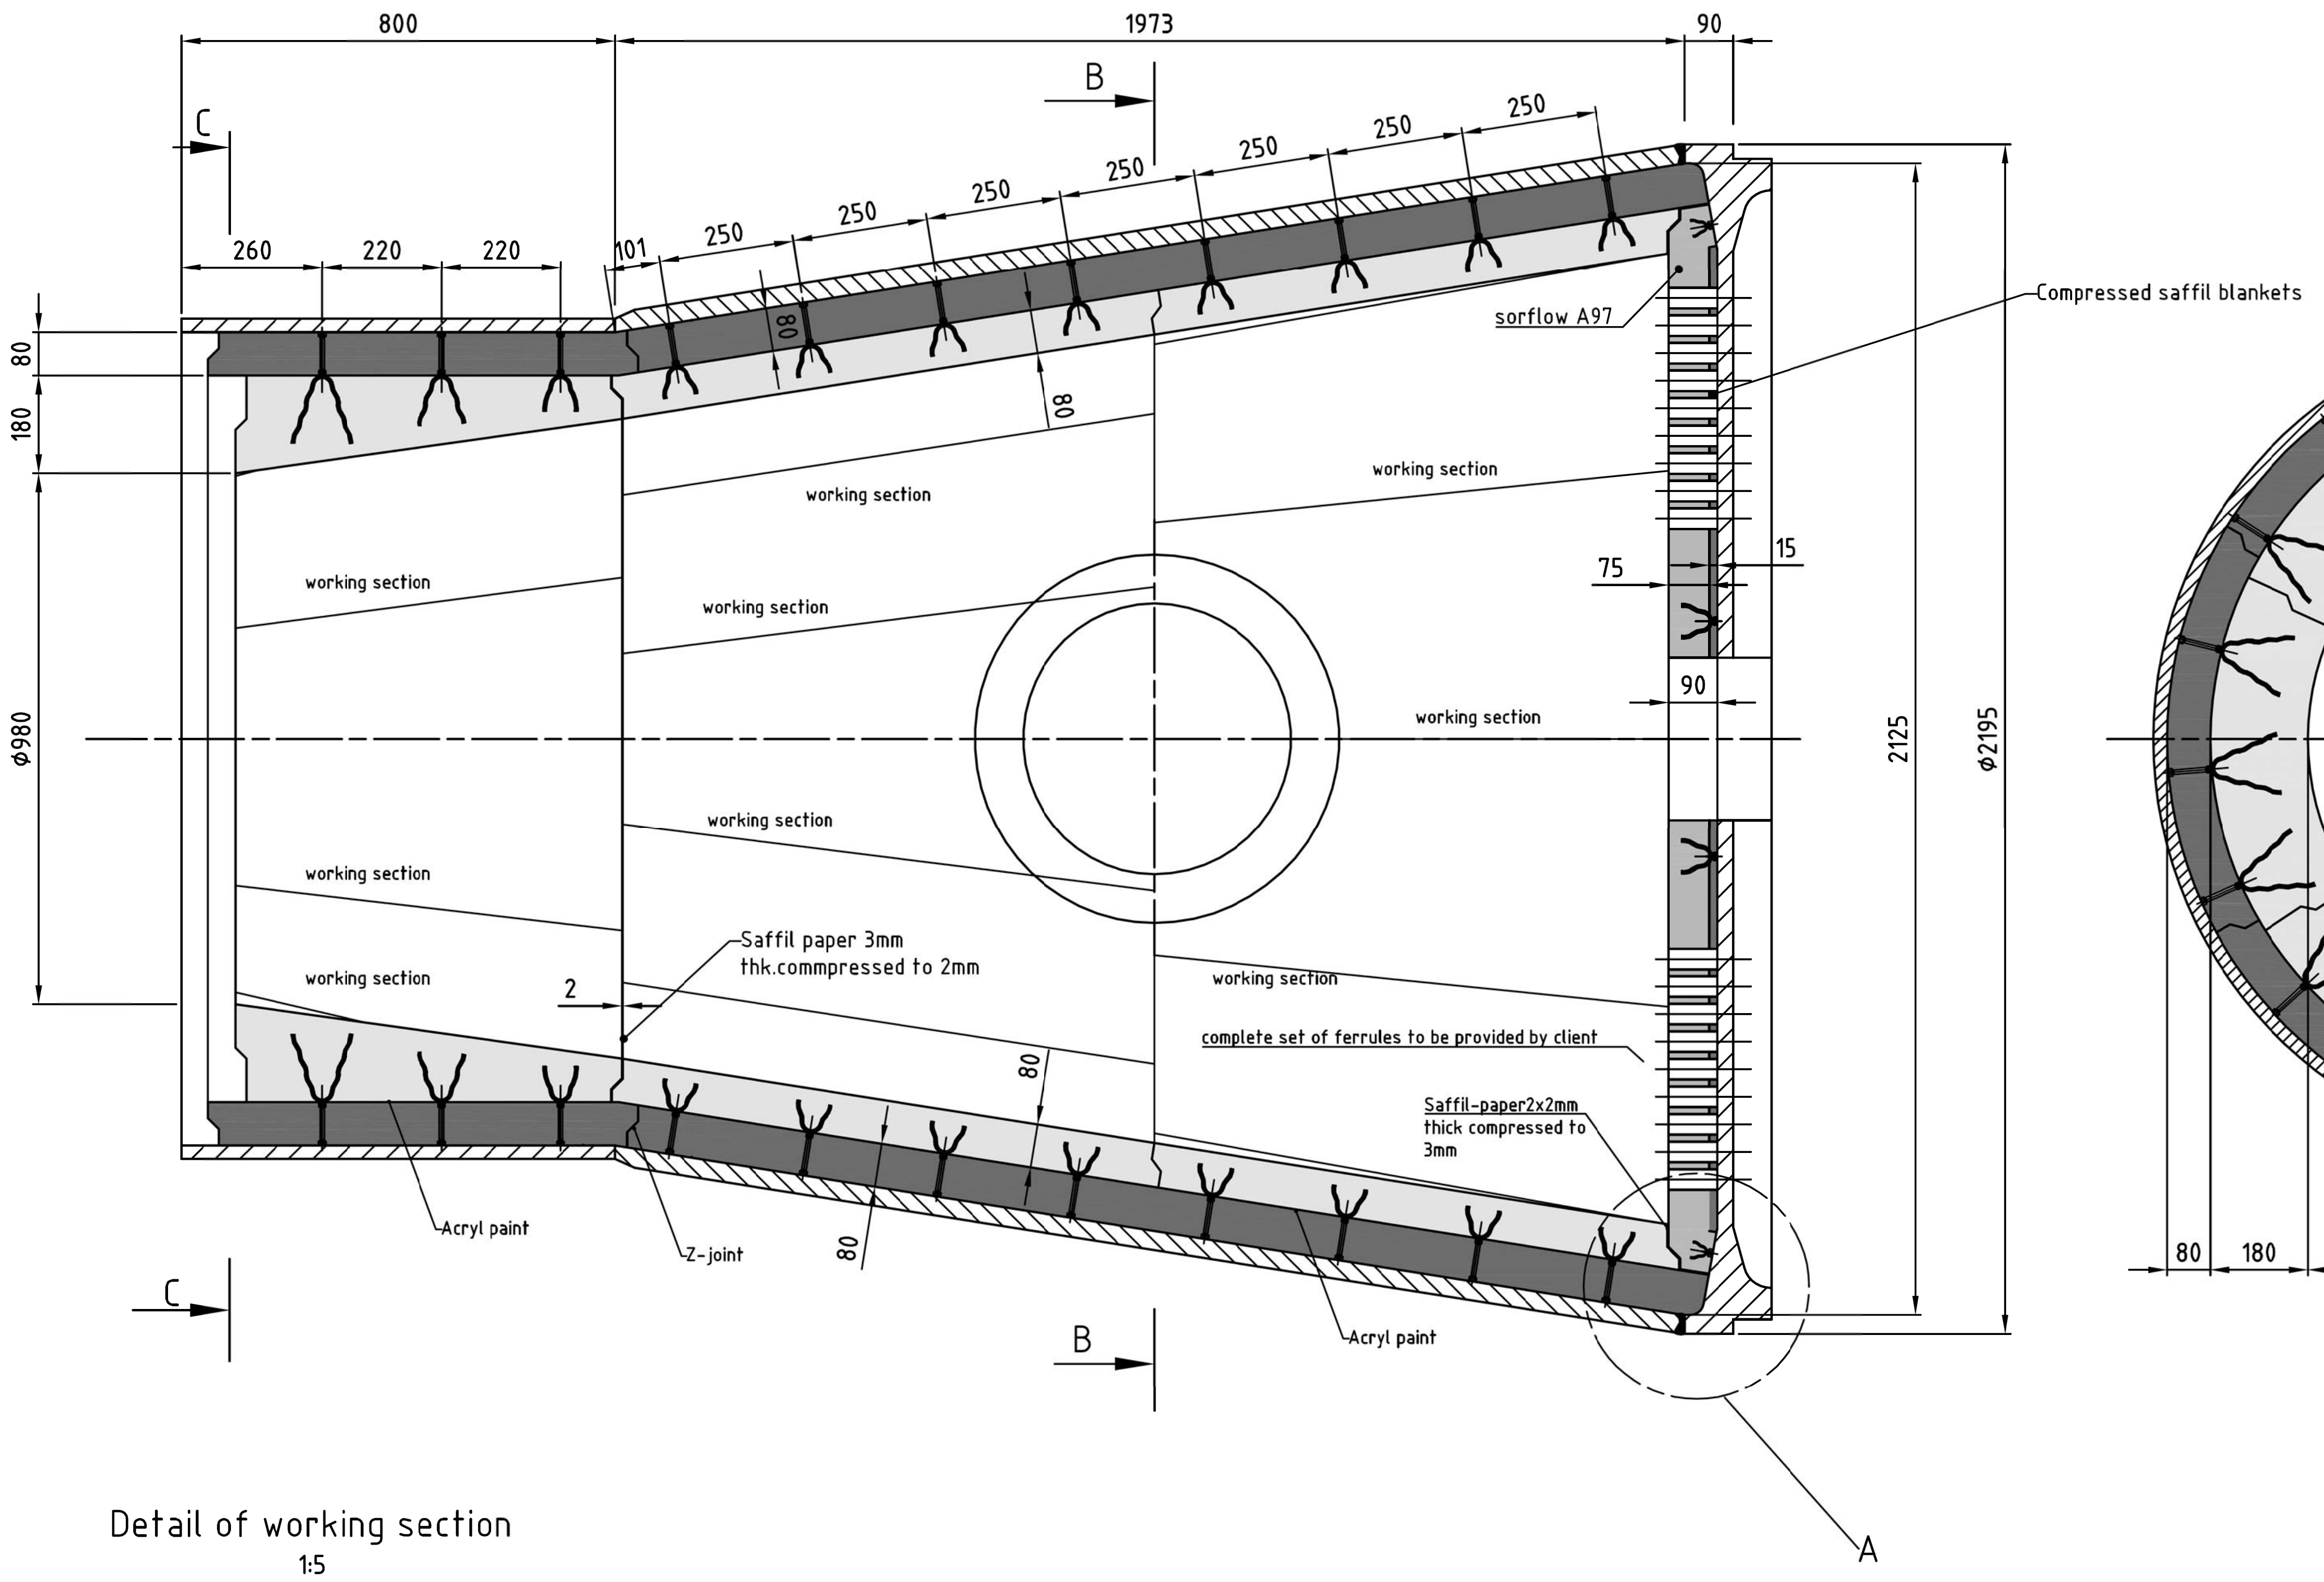

800
1973
90
C
B
260
220
220
101
250
250
250
250
250
250
250
250
80
180
ø980
80
80
sorflow A97
Compressed saffil blankets
working section
working section
working section
working section
working section
working section
working section
working section
working section
75
15
90
2125
ø2195
Saffil paper 3mm thk.commpressed to 2mm
2
80
complete set of ferrules to be provided by client
Saffil-paper2x2mm thick compressed to 3mm
Acryl paint
Z-joint
80
Acryl paint
C
B
A

Section C-C

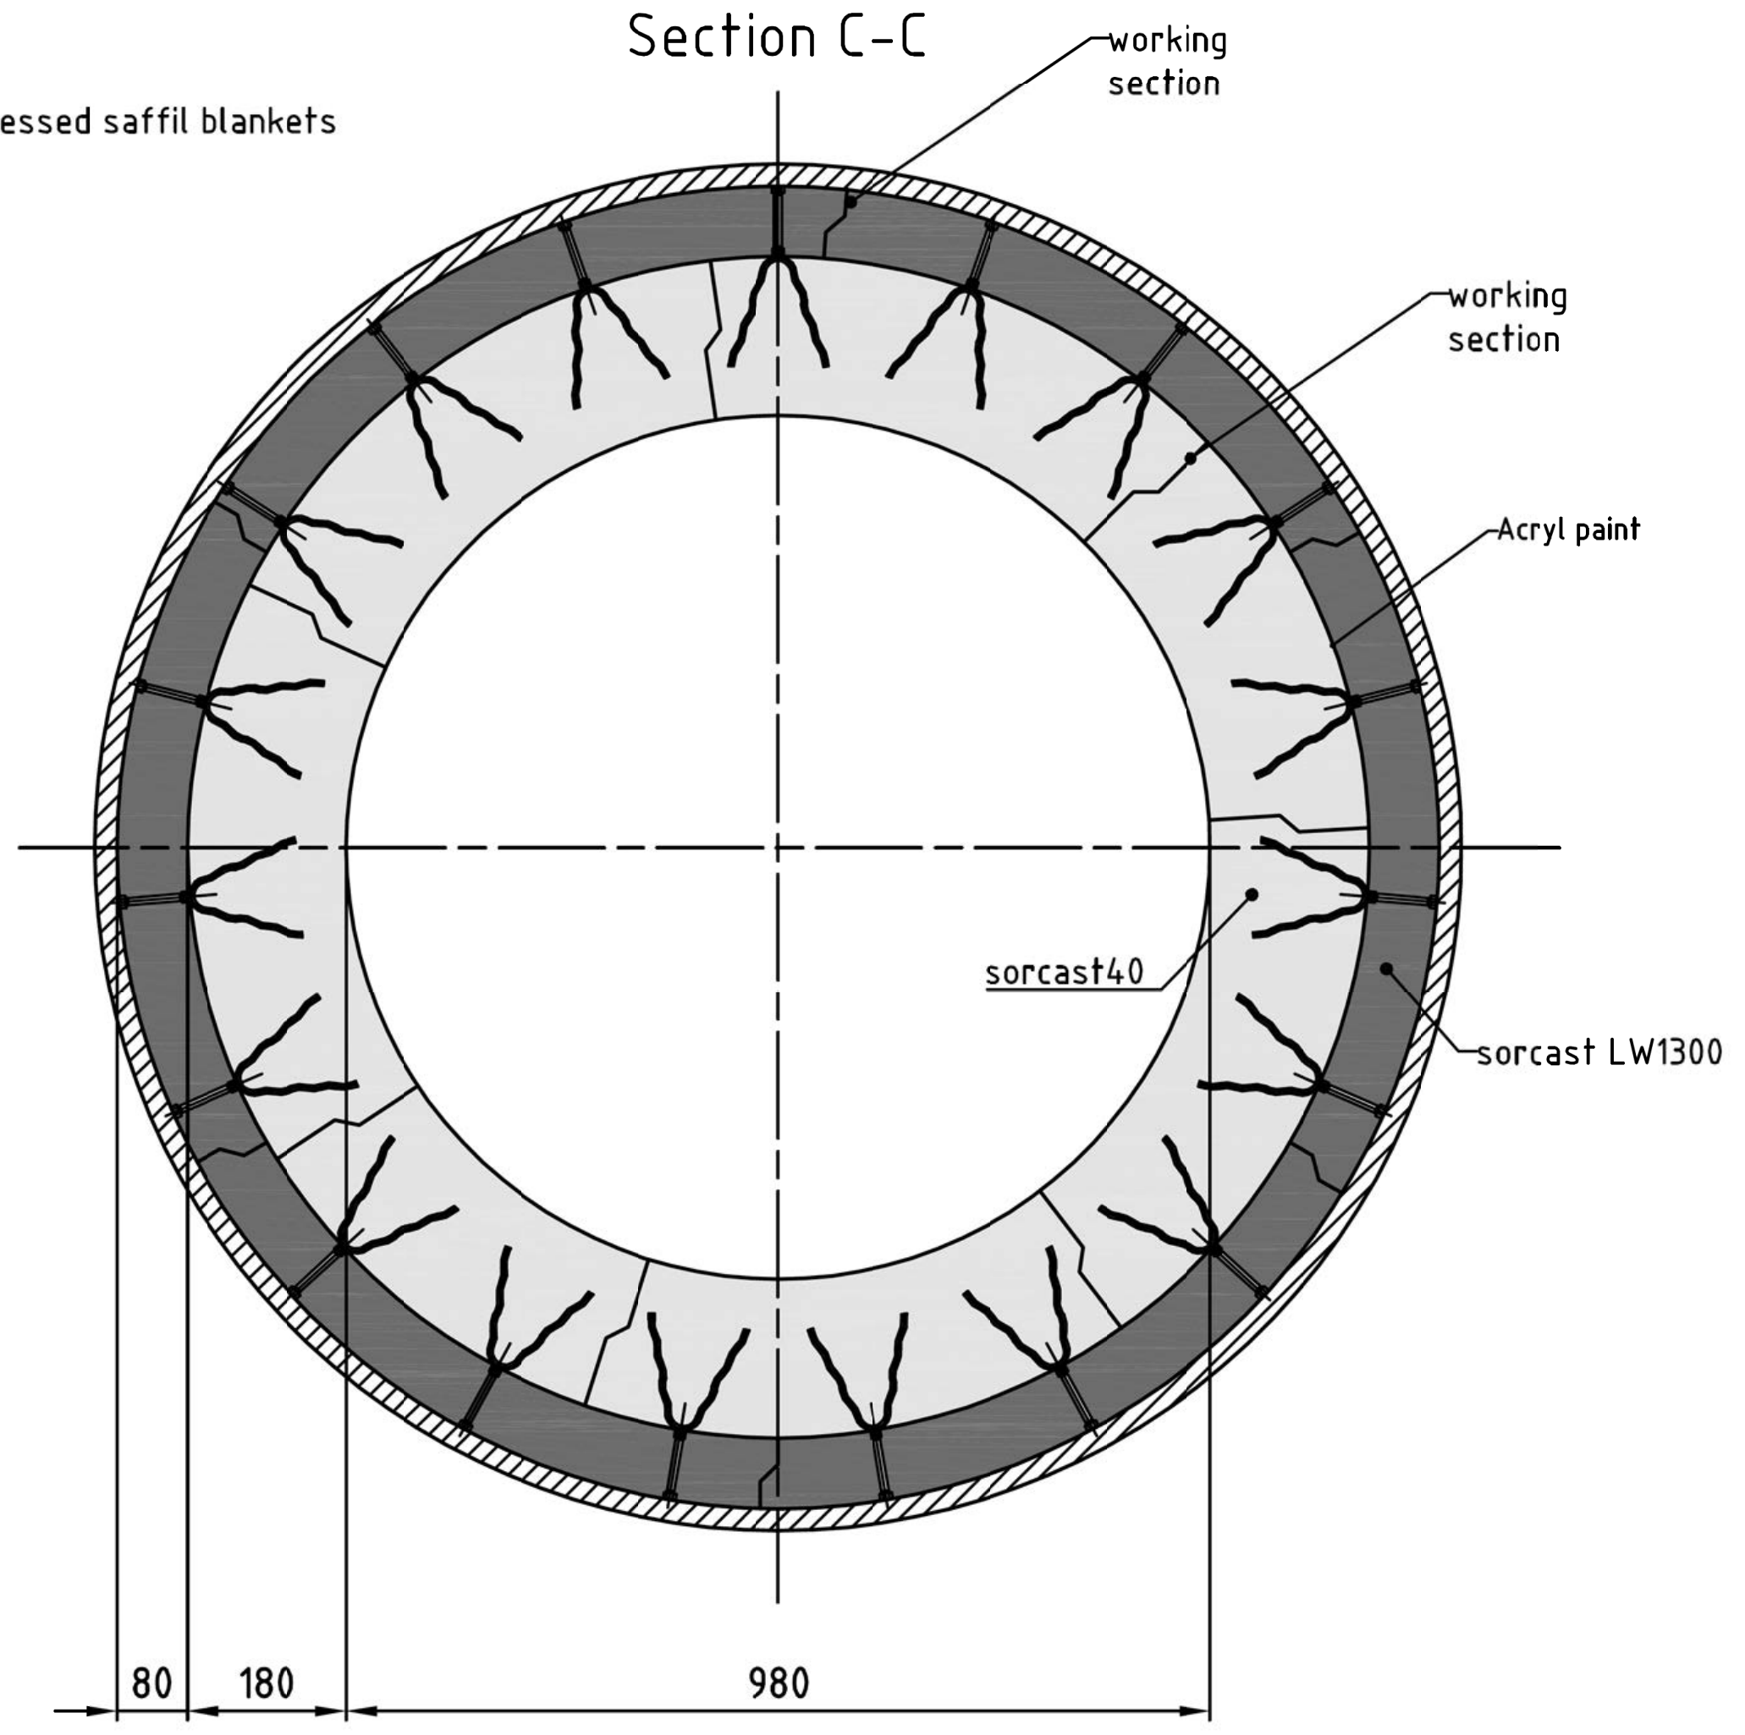

working section
working section
Acryl paint
sorcast40
sorcast LW1300
80
180
980

Section B-B

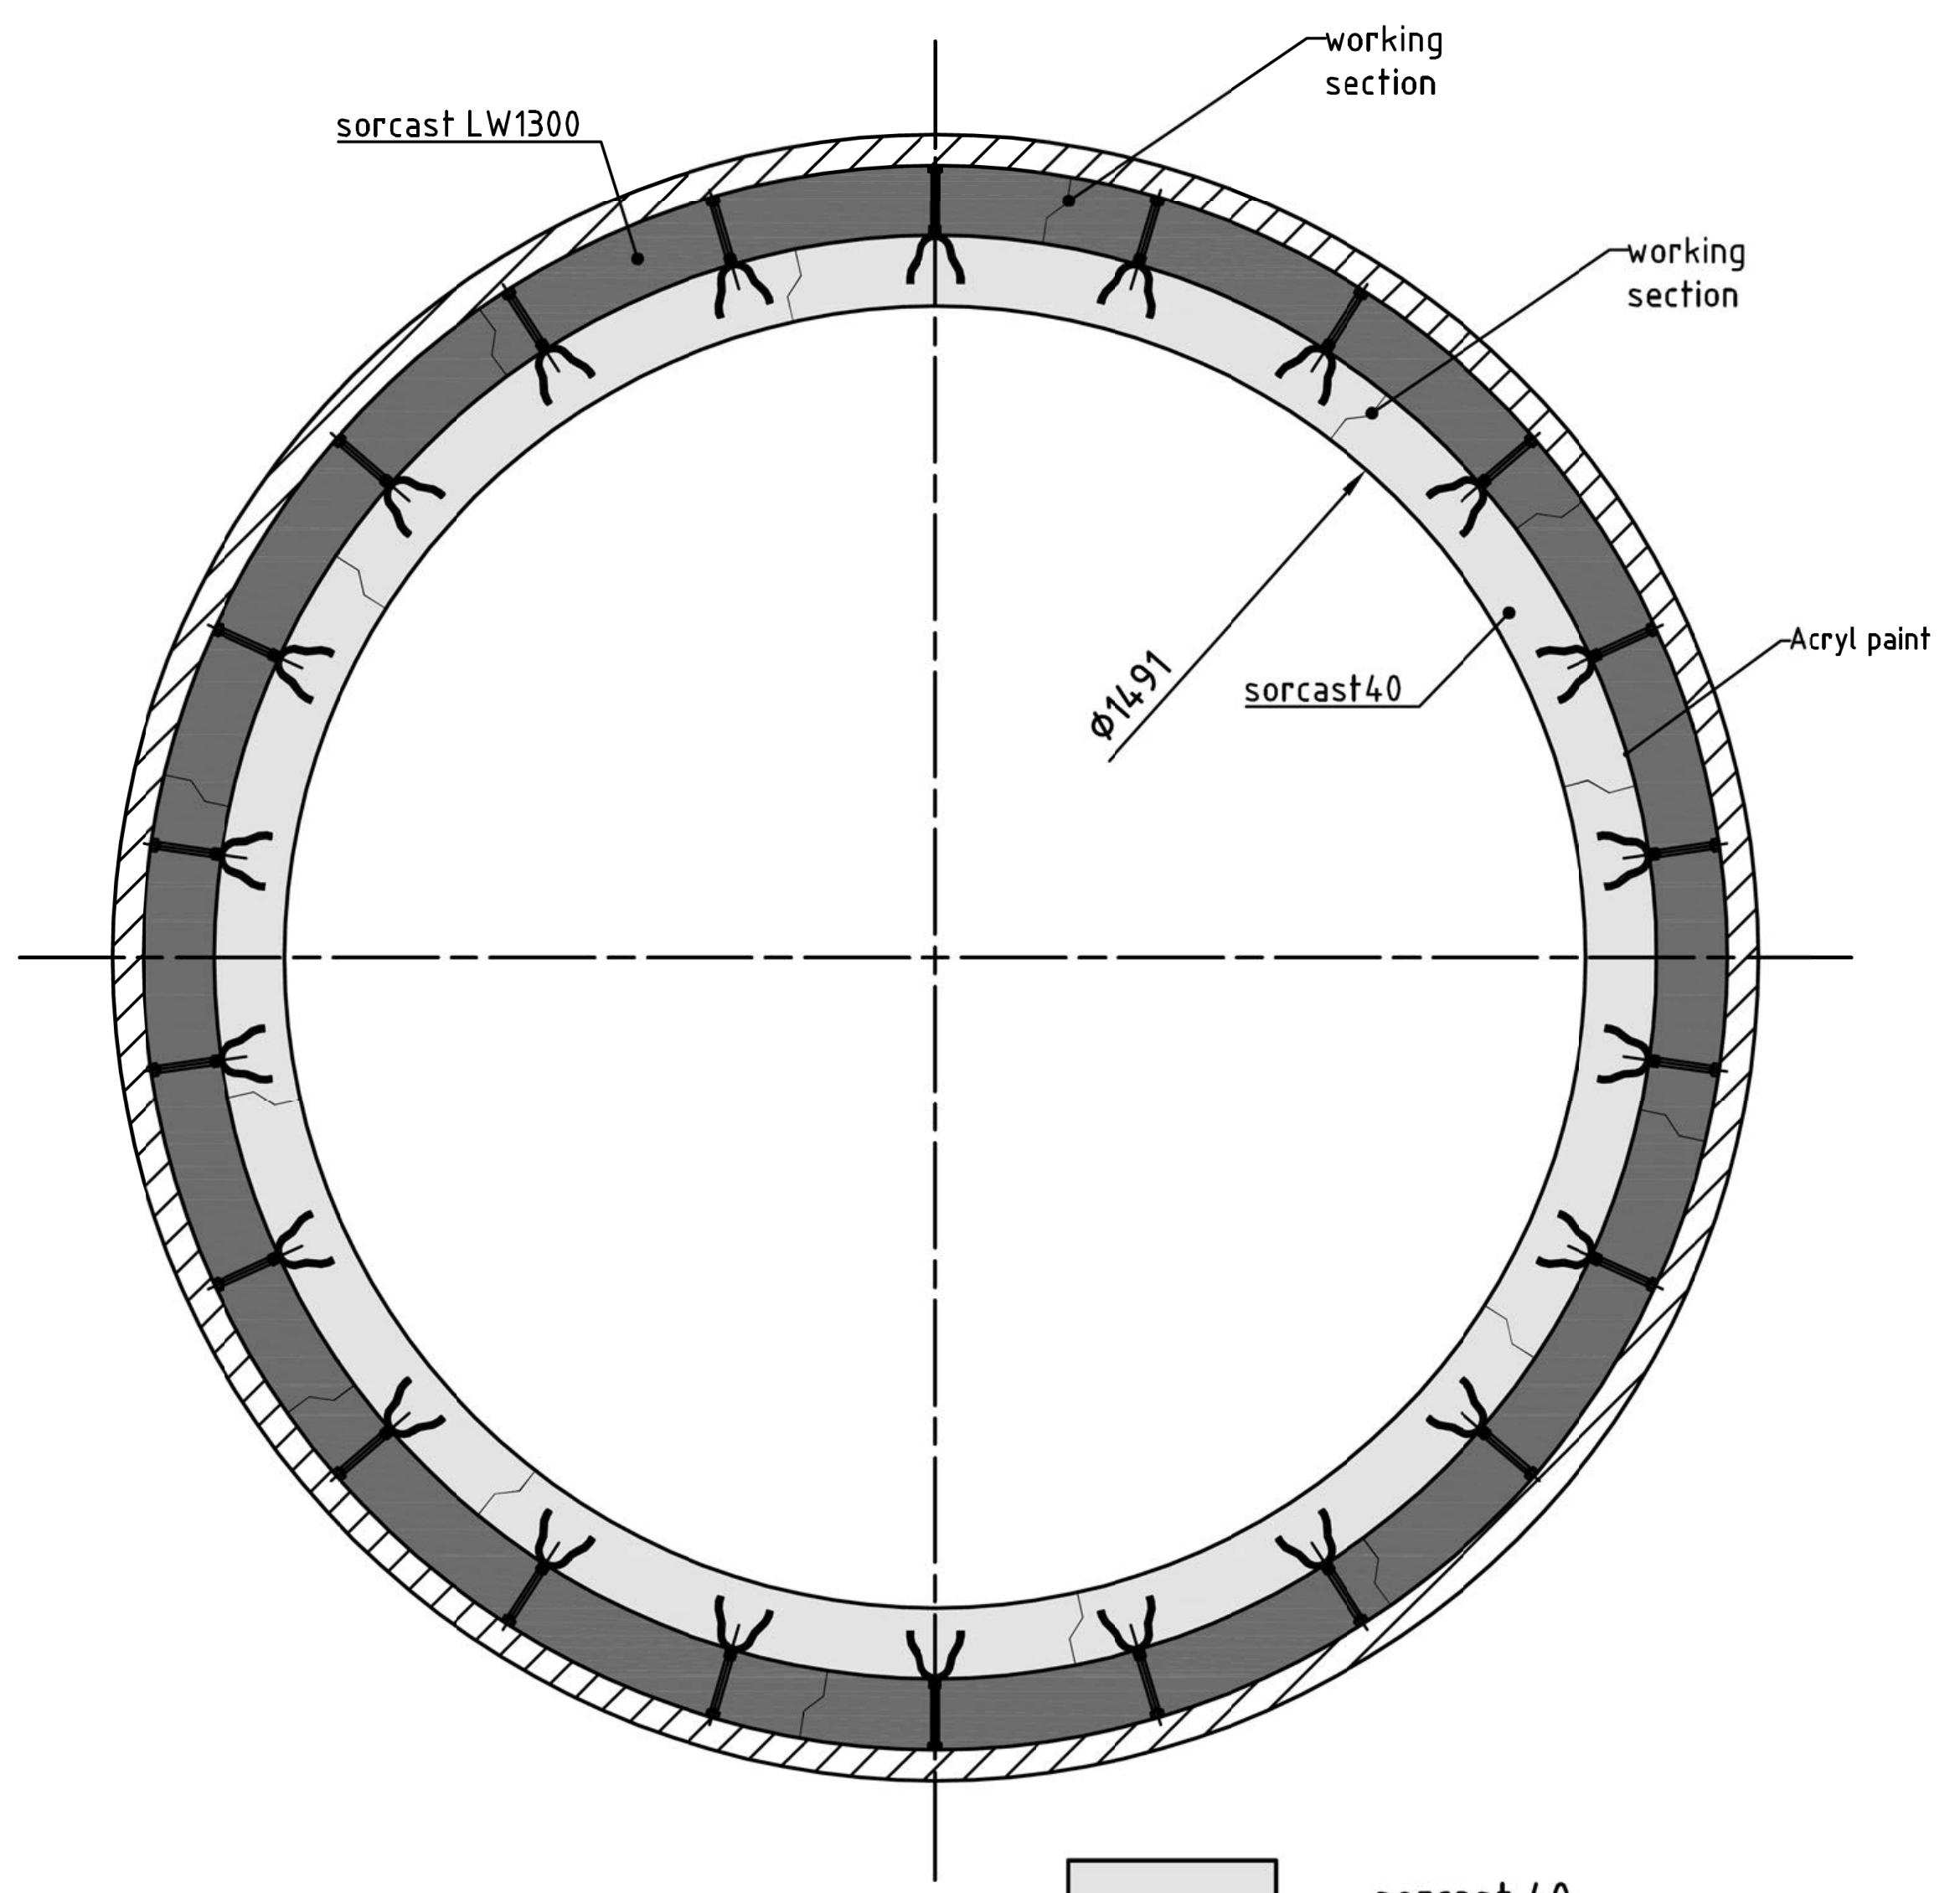

sorcast LW1300
working section
working section
ø1491
sorcast40
Acryl paint

▨ sorcast 40

▨ sorcast 40 Pre-Cast Shapes

▨ sorflow A97_1

▨ sorcast LW1300_1

▨ sorcast LW1300 Pre-Cast Shapes

▨ Compressed Saffil blankets

▨ Saffil Paper

Detail of working section

1:5

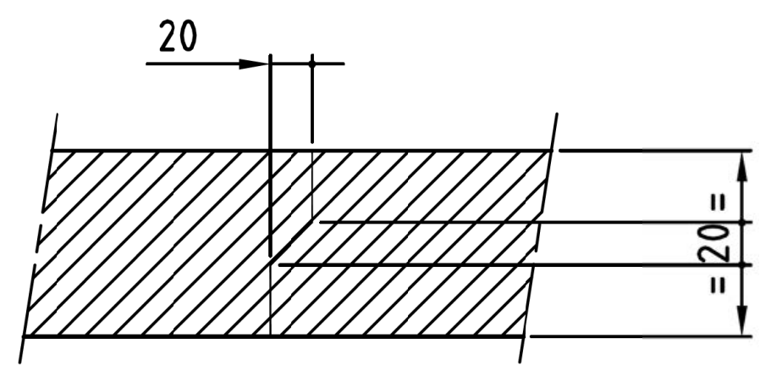

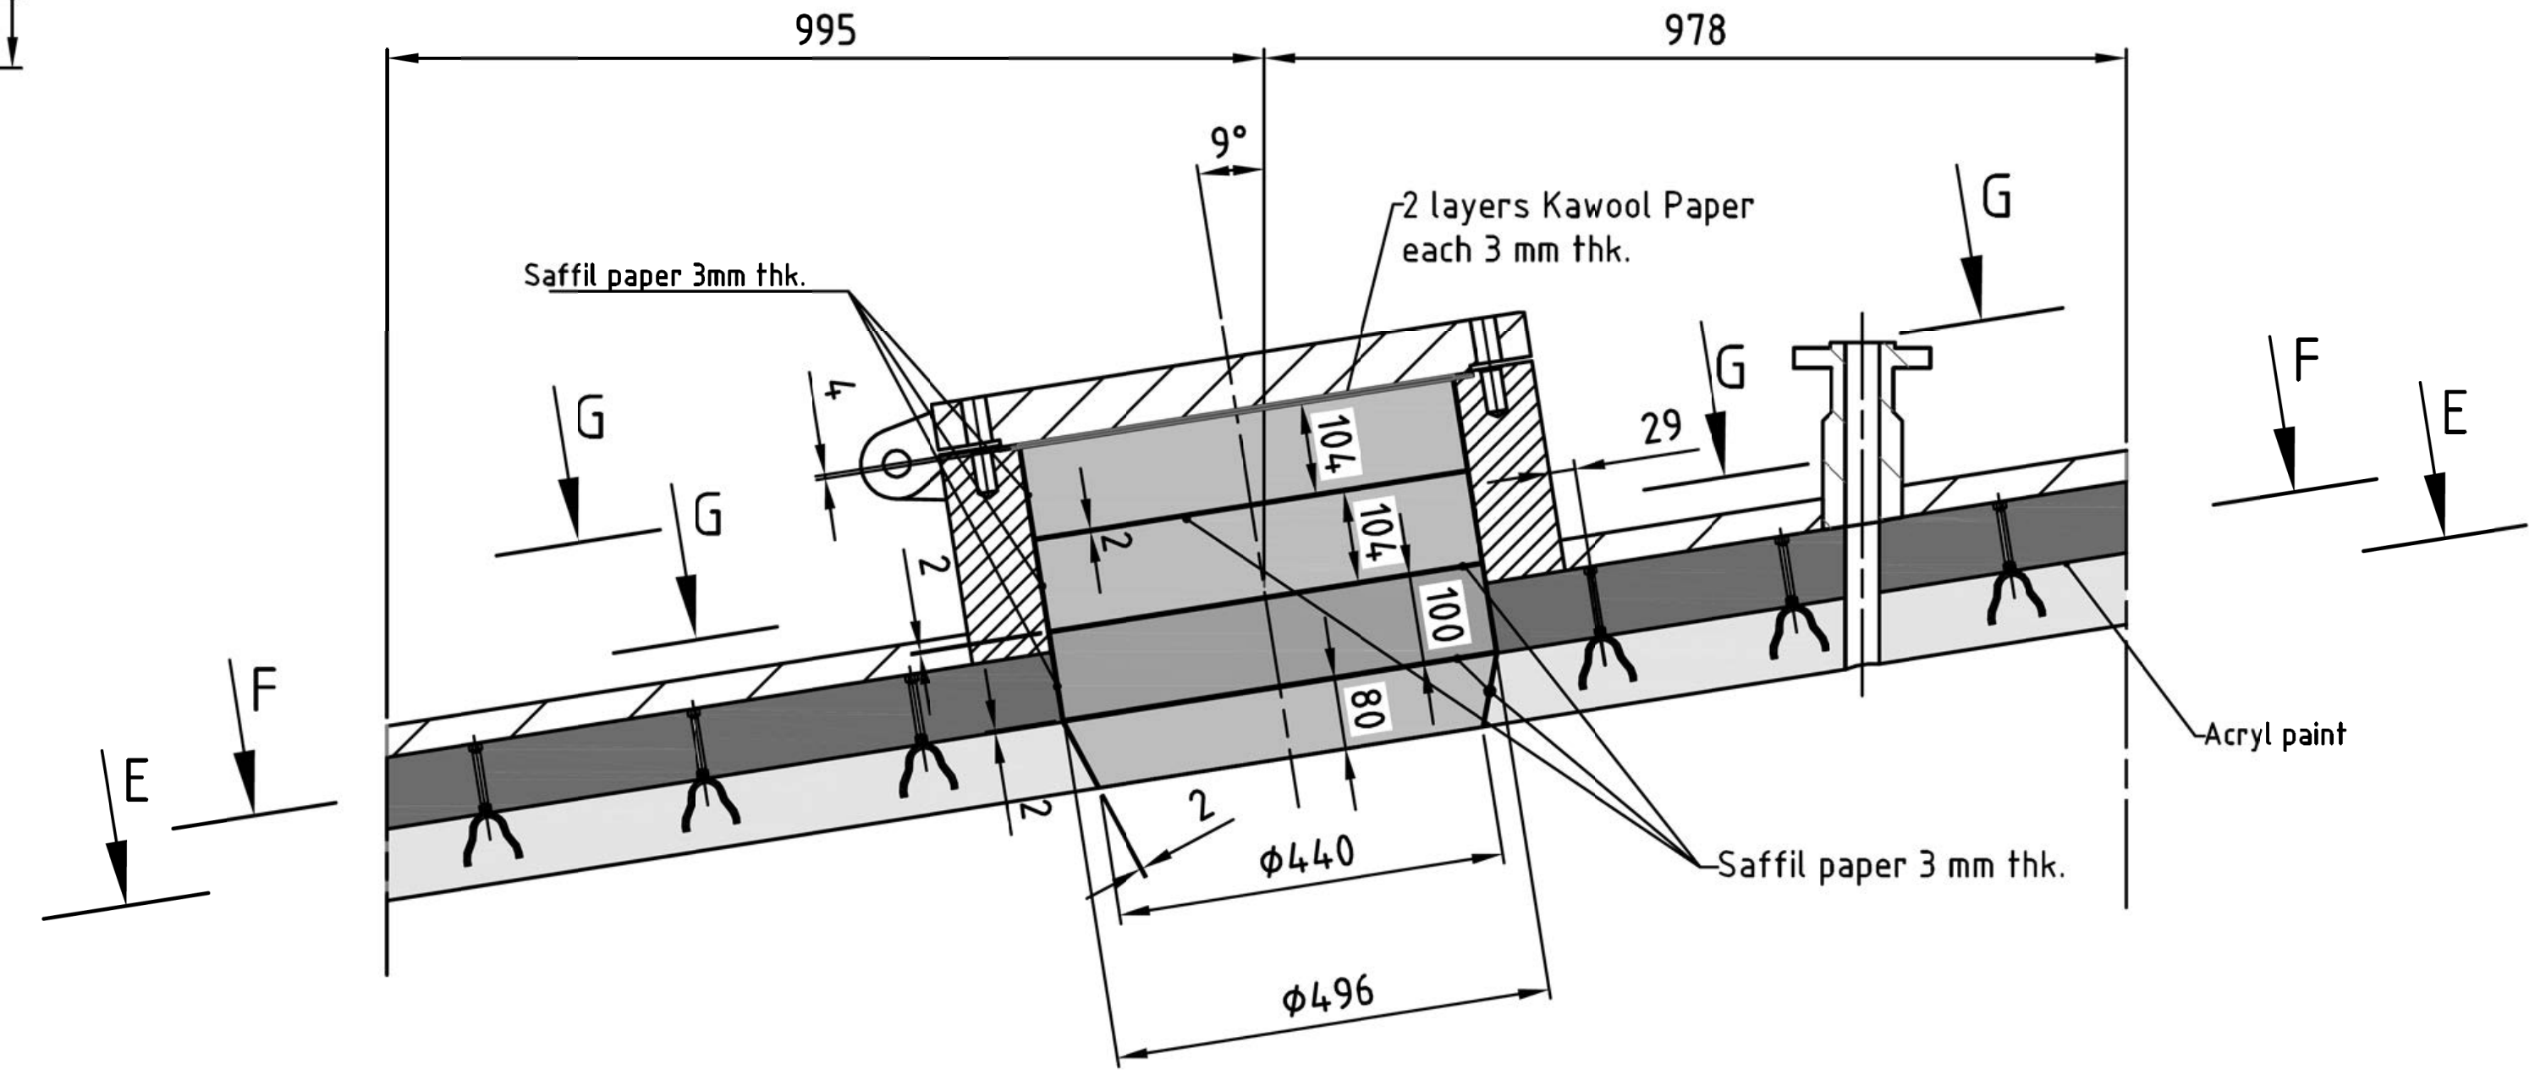

995
978
9°
Saffil paper 3mm thk.
2 layers Kawool Paper each 3 mm thk.
G
G
G
G
4
104
104
100
80
2
2
2
2
29
F
E
F
E
ø440
ø496
Saffil paper 3 mm thk.
Acryl paint

Section E-E

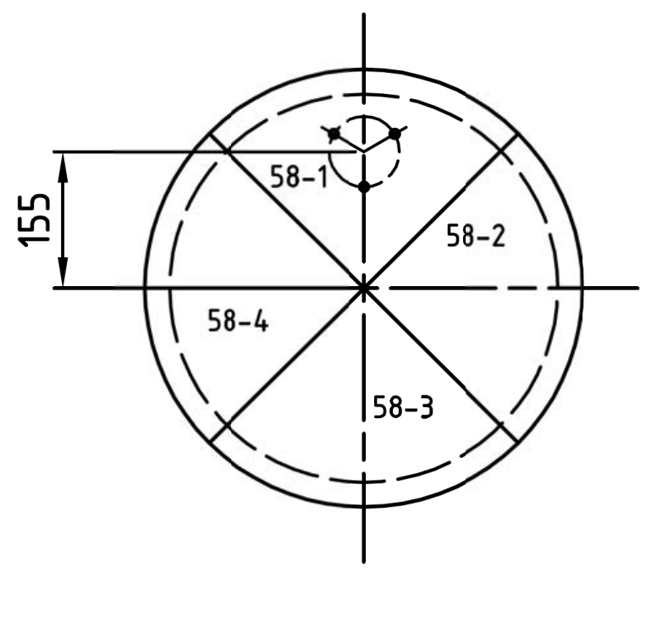

155
58-1
58-2
58-4
58-3

Section F-F

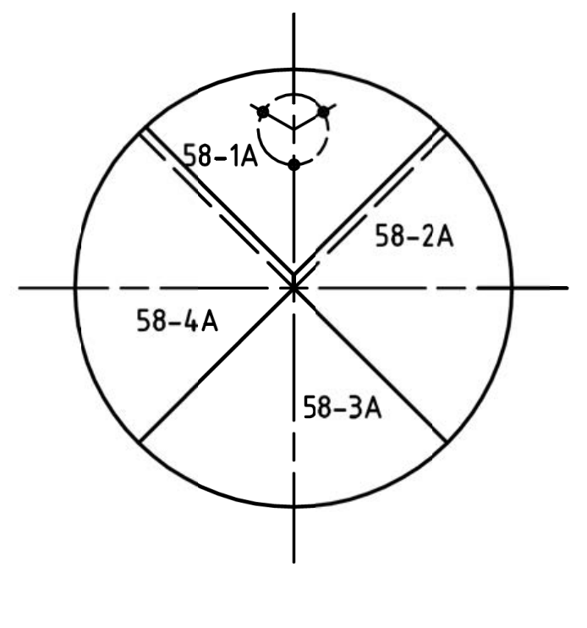

58-1A
58-2A
58-4A
58-3A

Section G-G

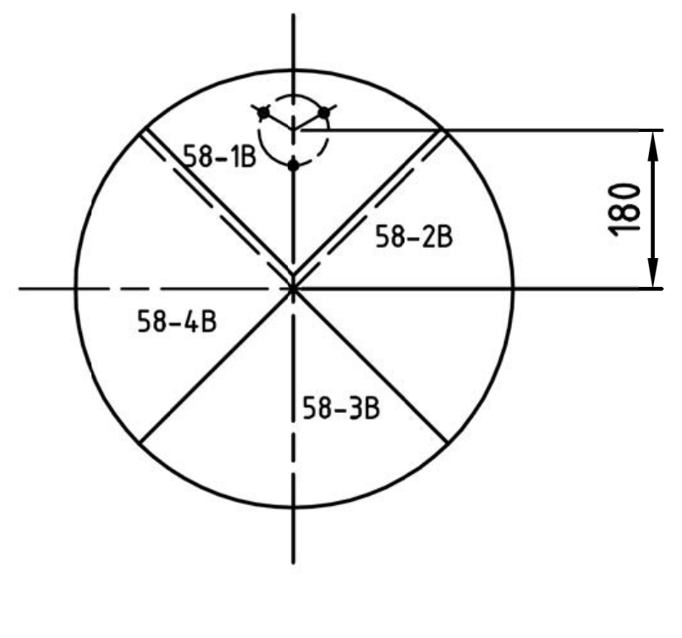

58-1B
58-2B
58-4B
58-3B
180

Detail A

1:5

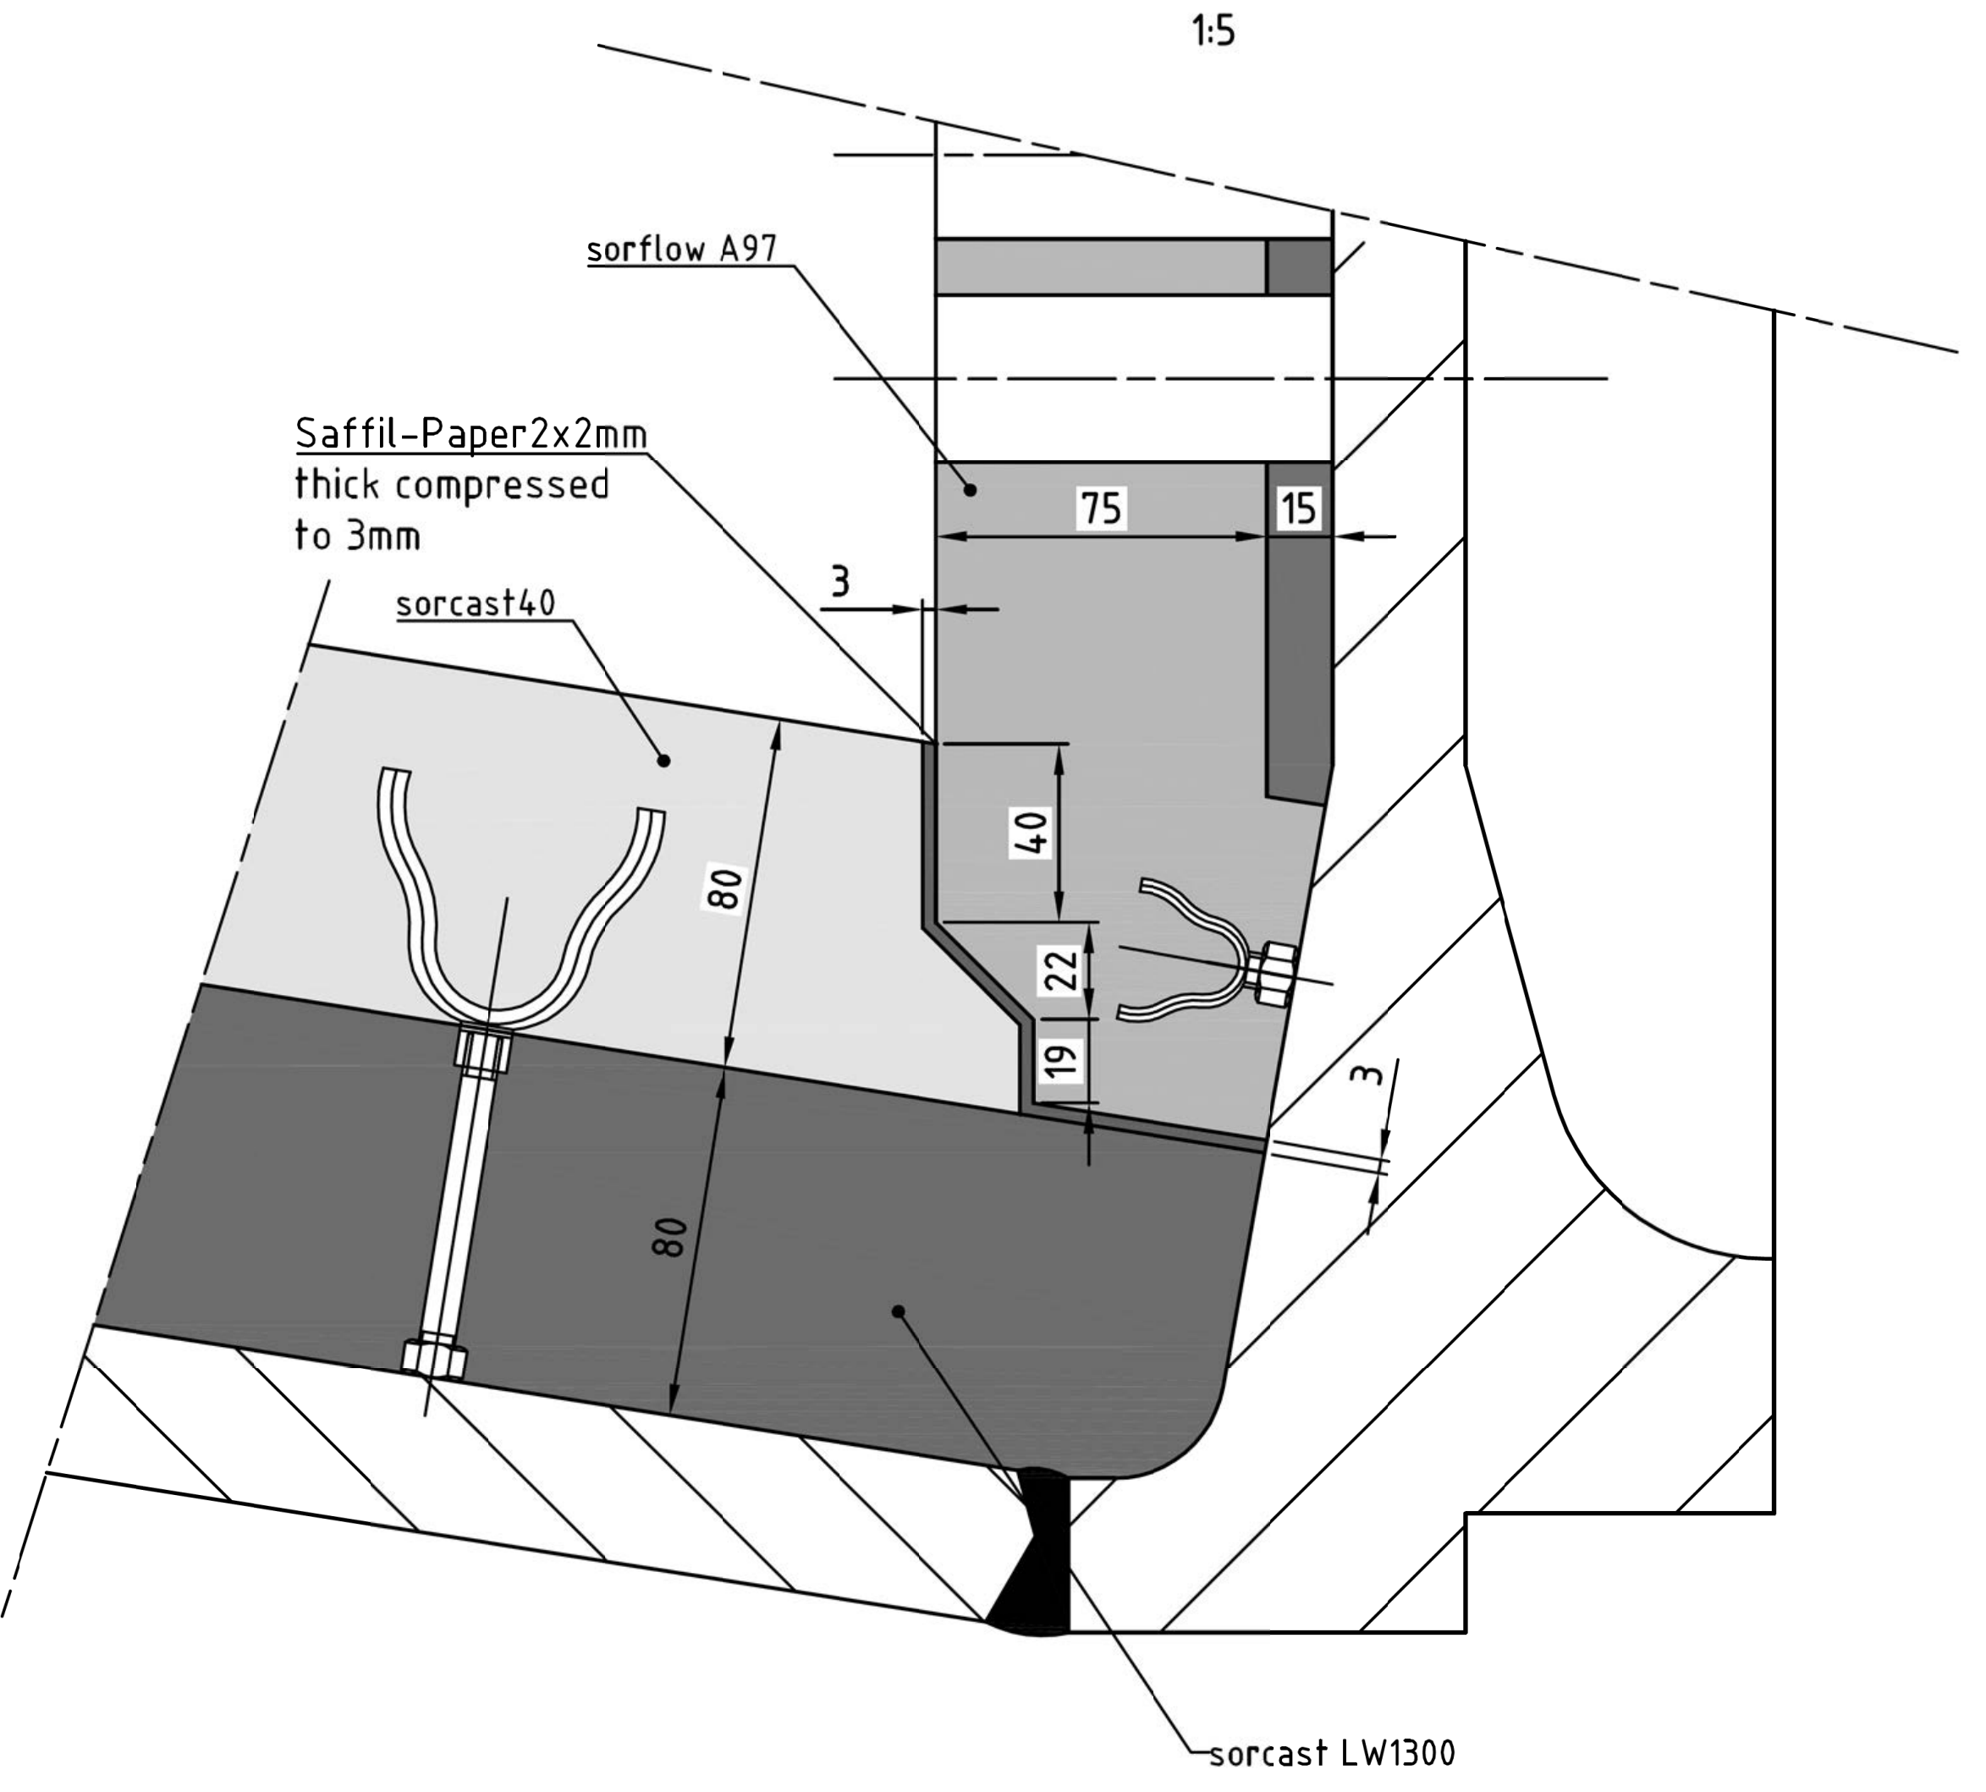

sorflow A97
Saffil-Paper2x2mm thick compressed to 3mm
sorcast40
75
15
3
40
22
19
3
80
80
sorcast LW1300

Revision	Date	Name	Description
A	06.04.2014	Esser	modification tube sheet wall

Sec. Reformer Effluent Waste Heat Boiler

Refractory Linings - General Arrangements and Details

Euro. Projection	Scale	Project No.	Drawing	Group	Drawing No.	Page	of	Revision	Format
	1:5	13-02-0059			13-02-0059-0002			A	A0

	Date	Name	Customer No.
Drawn	10.03.2014	Esser	PRT/ASH

SRS

Wolske
APPROVED

NO COMMENT

3:16 pm, Jul 12, 2014

By: seraj.mohammad

HEDCO

SUISIO - BERGAMO - ITALY

CUSTOMER }

ORDINE CLIENTE PURCHASE ORDER } FZMC-13450-R1

IMPIANTO E LOC. LOCATION & UNIT } Ammonia Urea Project

SERVIZIO SERVICES } Sec. Reformer Effluent Waste Heat Boiler

TITOLO TITLE } Internal refractory

SCALA/FORMATO SCALE/FORMAT	NO / A1	TIPO / TEMA / TYPE	NUMERO APPAR. NUMBER REQUIRED	SIGLA / ITEM No.
DATA DATE	15/05/14	BXM SPEC.	} 1	3-E-1401
DISEGNATO DRAWN.	Esser			
CONTROLL. CHECKED	Sarti			
APPROVATO APPROVED	Sarti			

DIMENSIONI / SIZE	NUM. DI FABBRICA SERIAL NUMBER	ANNO DI COS. YEAR OF CONS.	COMM. / JOB	NUM. DIS. / DWG. NUM.	REV.
13000 x 2025	12542	2014	7523	7523-01-600-01	0

REV.	ISSUE DATE	DESCRIPTION	DWN. BY	CHKD. BY	APPR. BY	APPR. BY
1	05/14	ISSUED FOR APPROVAL	E	W	S	

OWNER: LORDEGAN PETROCHEMICAL COMPANY

Project: LORDEGAN AMMONIA AND UREA PROJECT

CONTRACTOR : HAMPA ENGINEERING CORPORATION

DETAIL ENGINEER : HEDCO Hampa Energy Engineering & Design Company

SUISIO - BERGAMO - ITALY

TITLE : INTERNAL REFRACTORY 3-E-1401

Project No:2103	HAMPA	Doc. No.	7523-01-000-01	REV.
Scale: Sheet of	Vendor		2103-A-VD-255-A1-MD-029	0

THIS DRAWING AND THE DESIGN IT COVERS IS THE PROPERTY OF LORDEGAN PETROCHEMICAL COMPANY AND ALL RIGHTS ARE RESERVED. NEITHER IN WHOLE NOR IN PART MAY BE REPRODUCED OR TRANSMITTED TO THIRD PARTY WITHOUT PRIOR WRITTEN CONSENT OF OWNER.

OWNER : LORDEGAN PETROCHEMICAL COMPANY

PROJECT TITLE : LORDEGAN AMMONIA AND UREA PROJECT

CONTRACTOR : HAMPA ENGINEERING CORPORATION

DETAIL ENGINEER : HEDCO Hampa Energy Engineering & Design Company

P.O. NO. : 2103-POR-A-HM-255

REQ NO. : 2103-REQ-A-HM-255

DOC. NO. 2103-A-VD-255-A1-MD-029

ITEM NO. : 3-E-1401

Rev. 0

NC – REVIEWED WITH NO COMMENT

C – DO NOT PROCEED WITH FABRICATION

AC – APPROVED WITH MINOR COMMENTS

RE – DOCUMENT WAS NOT ACCEPTED

DEPARTMENT :

DATE:

PERSON IN CHARGE :

Purchaser's permission to proceed or review taken on vendor prints shall not relieve vendor from its responsibilities or liabilities under purchase order.